

	HINDUSTAN SHIPYARD LIMITED (A Govt. of India Undertaking) Ministry of Defence Gandhigram, Visakhapatnam - 530005	Electrical Design	REV: 001
		Yard No: 11190-91	DATE: 26.08.2020
		SPT	Page 1 of 25



SHIP BUILDER
HINDUSTAN SHIPYARD LIMITED
 VISAKHAPATNAM- 530005.

TECHNICAL SPECIFICATION FOR PROCUREMENT OF SOUND POWERED TELEPHONE SYSTEM

Project	:	DIVING SUPPORT VESSEL VC 11190 – 91
CLIENT	:	IHQ MOD (N) / DSP
DOCUMENT No	:	HSL/DSV/EL/SOTR/009

	HINDUSTAN SHIPYARD LIMITED (A Govt. of India Undertaking) Ministry of Defence Gandhigram, Visakhapatnam - 530005	Electrical Design	REV: 001
		Yard No: 11190-91	DATE: 26.08.2020
		SPT	Page 2 of 25

001	Incorporated IHQ, MoD (N) comments, Letter Dtd. 13 Aug 20	26.08.2020	R.Sreenu	B. Ravi Kumar
000	First Issue to IHQ, MoD (N)	27.06.2020	R.Sreenu	B. Ravi Kumar
REV	DESCRIPTION	DATE	Prepared By:	AUTHORISED BY

LIST OF CONTENTS:

CHAPTER	DESCRIPTION	PAGE No.
1	Preamble	3-5
2	Functional Requirements	5-6
3	System Configuration	6-7
4	Scope of Supply	7
5	Technical Requirements	7-10
6	General	10-12
7	Spares, Tools and Test Equipment	12-13
8	Binding Data, Design Drawing & Technical Documentation	13-16
9	Quality Assurance	16
10	Inspection & Testing	16-18
11	Other terms and Conditions	18-20

LIST OF ANNEXURES:

1	ANNEX-1 : Format for Manufacture's recommended spares, tools, software(MRL-OBS) and Base & depot spares (ILMS Format)	21-23
2	ANNEX-2 : Documentation Format	24-25
3	ANNEX-3 : SLD of Sound Powered Telephone	26-39

	HINDUSTAN SHIPYARD LIMITED (A Govt. of India Undertaking) Ministry of Defence Gandhigram, Visakhapatnam - 530005	Electrical Design	REV: 001
		Yard No: 11190-91	DATE: 26.08.2020
		SPT	Page 3 of 25

Chapter 1 - Preamble		
Clause No.	Description of Technical Specification	Vendor Reply Complied /Not Complied
1.1	This document defines the technical requirements for design, development, manufacture, supply, testing, installation, setting to work, trials and onboard commissioning of sound powered telephones complete with associated accessories and fitted on suitable mounts for 2Nos. of Diving Support Vessels (DSV) class of ships.	
1.2	The system is designated as Sound Powered Telephone and should be referred to SPT / SP telephones, as such.	
1.3	System Overview: The SP Telephone to be designed to offer an easy to use, low maintenance communications facility, ideally suited to emergency or secondary communication applications. The SP telephones should be technologically upgraded one to realize quality audio with pre amplifier working on chargeable capacitor battery. The capacitor battery charged by the call generator (by cranking) provides power to the integral amplifier for up to 20 minutes of operation. The hand operated generator to initiate a low frequency pulse DC calling signal, which is converted at the receiving telephone into ringing tone. The SP Telephone systems should have multi-way selection facility amongst users within a functional line.	
1.4	System Feature: SP Telephone, an emergency communication set will be catered for various positions as detailed in the SPT SLD at Annex-3. Those SPTs, being multiway type any position can communicate with all other positions within a functional line. The SP Telephone system will have the following major features (a) SPT system should provide loud and clear voice communication between key locations on a ship for both emergency and routine communication. Excellent speech quality to be achieved by integrated pre-amplification circuits & microphone with dynamic noise canceling and negligible power loss over cabling. (b) SPT should be light, robust and corrosion resistant and will be suitable for all on-board naval environment. (c) SPT system should operate independently without ships/ external power supply and provide seamless voice communication during emergency conditions. SPT will have a provision for connecting the ships emergency DC supply (24V) and should be able to operate as conventional external powered telephone system, thereby avoiding the	

	HINDUSTAN SHIPYARD LIMITED (A Govt. of India Undertaking) Ministry of Defence Gandhigram, Visakhapatnam - 530005	Electrical Design	REV: 001
		Yard No: 11190-91	DATE: 26.08.2020
		SPT	Page 4 of 25

	use of hand cranking and to work as a battery telephone system. (e) SPT system should have internal systems/ circuitry to amplify the voice signals and able to transmit/receive voice signals between the other SPTs installed onboard. (f) The SPTs control box is to be equipped with visual (LED) and audible call indication. The audible call and LED indication should be prominent till a distance of at least 10 m from the unit during ship's operating phases. Suitable indications to be provided to identify caller and select a particular user for calling is required to be provided in the SPT control box. (g) SPT system should have noise compensated headsets with noise compensated microphones that can be connected to a plug/socket box fitted in the SPT system network. Headset directly to be connected to the telephone station or connected to a portable Telephone via plug box. (h) The SPT system should have plug/socket box for connecting the portable SPTs and portable headsets. The location and number of plug / socket box required for connecting the portable SPT / headsets. (i) The SPT system should have audio and visual combined flash alarm units. These units will be connected to the individual SPTs. The requirements of audio and visual combined flash alarm units in the SPTs as indicated in Annexure. These alarm units will be interfaced with the individual SPT directly or through a relay box. (j) The SPT system has number of variants with different configurations Viz single way, multiway. The SPT system should provide the means to select one of the various positions with which the user may need to communicate. (k) The SPT system should have group isolation (Anchoring group, Conning and Steering group, Electrical & communication group, Machinery group, Helo & AVCAT group, Diving & DP group and Damage Control Group) and one group should be able to communicate with the SPTs of other groups. Call Conference facilities maximum upto 08 SPT should be available. (l) The SPT system for new constructions ships should have screened cable, network for interconnection between SPTs. (m) The SPT and associated accessories should meet the ingress	
--	---	--

	HINDUSTAN SHIPYARD LIMITED (A Govt. of India Undertaking) Ministry of Defence Gandhigram, Visakhapatnam - 530005	Electrical Design	REV: 001
		Yard No: 11190-91	DATE: 26.08.2020
		SPT	Page 5 of 25

	protection based on locations where it is going to be fitted. For SPTs fitted in the weather Decks should have IP66 rating for underwater compartments it should have IP67 rating and for other locations it should have IP55 ratings. The enclosure should be an aluminum or steel or alloy or composite materials having suitable arrangements for deck head/ Bulkhead mounting type installation on-board ships. (n) If one SPT is sited inside a hazardous area, the SPTs shall meet the degree of intrinsic safety required for hazardous areas, thus preventing dangerous voltages being introduced into the hazardous area by telephones/ Circuits of the SPT system network sited outside the area.	
	Chapter 2 - Functional Requirements	
2.1	The Supplied SPT shall have the following major features: - (a) SPTs shall provide load and clear voice communication between key locations on the ship for both emergency and routine communication. Excellent speech quality shall be achieved by integrated pre-amplification circuits and negligible power loss over cabling. (b) The SP Telephones are Light & Robust and to be housed in a corrosion and impact resistant casing which can be desk-top, bulkhead or with an optional mounting kit for console mounting. (c) SPTs shall be multiway type with selection switch for selecting users (i.e. flexibility in operation). Any user shall be able to communicate with all other users within a functional line. (d) SPT system shall be able to operate independently without ship's/external power supply and provide seamless voice communication during emergency conditions. SPTs shall have a provision for connection to ship's DC supply (24V) and operate as a conventional external powered telephone system, thereby avoiding use of hand cranking. (e) SPTs shall be equipped with visual (LED) and audible call indication. The audible call and LED Indication shall be prominent up to 10M distance from the unit during ship's operating phases. Suitable indications shall be provided for caller identification and selecting a particular user for calling. (f) SPTs shall have noise compensated headsets and noise compensated microphones connected directly to the SPT Stations as indicated in Annexure. (g) SPT system shall have group isolation between following groups as per table below:-	

	HINDUSTAN SHIPYARD LIMITED (A Govt. of India Undertaking) Ministry of Defence Gandhigram, Visakhapatnam - 530005	Electrical Design	REV: 001
		Yard No: 11190-91	DATE: 26.08.2020
		SPT	Page 6 of 25

	<table><tr><th>Group Name</th><th>Functional Description</th><th>No. of User Position</th><th>JB Requirement</th></tr><tr><td>A</td><td>Anchoring, towing & docking</td><td>3</td><td>Dedicated JB</td></tr><tr><td>C</td><td>Conning and Steering</td><td>9</td><td>Dedicated JB</td></tr><tr><td>E</td><td>Electrical & Communication</td><td>17</td><td>Dedicated JB</td></tr><tr><td>M</td><td>Machinery</td><td>11</td><td>Dedicated JB</td></tr><tr><td>H</td><td>Helo & AVCAT</td><td>7</td><td>Dedicated JB</td></tr><tr><td>DI</td><td>Diving & DP</td><td>15</td><td>Dedicated JB</td></tr><tr><td>D</td><td>Damage Control</td><td>8</td><td>Dedicated JB</td></tr></table> <u>Inter-group Communication/connectivity is not desired</u>	Group Name	Functional Description	No. of User Position	JB Requirement	A	Anchoring, towing & docking	3	Dedicated JB	C	Conning and Steering	9	Dedicated JB	E	Electrical & Communication	17	Dedicated JB	M	Machinery	11	Dedicated JB	H	Helo & AVCAT	7	Dedicated JB	DI	Diving & DP	15	Dedicated JB	D	Damage Control	8	Dedicated JB	
Group Name	Functional Description	No. of User Position	JB Requirement																															
A	Anchoring, towing & docking	3	Dedicated JB																															
C	Conning and Steering	9	Dedicated JB																															
E	Electrical & Communication	17	Dedicated JB																															
M	Machinery	11	Dedicated JB																															
H	Helo & AVCAT	7	Dedicated JB																															
DI	Diving & DP	15	Dedicated JB																															
D	Damage Control	8	Dedicated JB																															
2.2	Supplied system shall meet the following major specification:- <table><tr><td>(a)</td><td>Construction</td><td>Enclosure shall provide high impact resistance, stability to ultra violet light and excellent chemical resistance.</td></tr><tr><td>(b)</td><td>Calling Signal Level</td><td>>75 dBA at 1 Meter or better</td></tr><tr><td>(c)</td><td>Switch</td><td>Magnetically operated reed switch</td></tr><tr><td>(d)</td><td>Audio level</td><td>-13 dBm or better</td></tr><tr><td></td><td>Mechanical requirements</td><td>Dimensional of SPT sets & JB's shall be kept as minimum as possible. Overall dimension, weight, proposed fixing arrangement etc. shall be indicated in the offer</td></tr></table>	(a)	Construction	Enclosure shall provide high impact resistance, stability to ultra violet light and excellent chemical resistance.	(b)	Calling Signal Level	>75 dBA at 1 Meter or better	(c)	Switch	Magnetically operated reed switch	(d)	Audio level	-13 dBm or better		Mechanical requirements	Dimensional of SPT sets & JB's shall be kept as minimum as possible. Overall dimension, weight, proposed fixing arrangement etc. shall be indicated in the offer																		
(a)	Construction	Enclosure shall provide high impact resistance, stability to ultra violet light and excellent chemical resistance.																																
(b)	Calling Signal Level	>75 dBA at 1 Meter or better																																
(c)	Switch	Magnetically operated reed switch																																
(d)	Audio level	-13 dBm or better																																
	Mechanical requirements	Dimensional of SPT sets & JB's shall be kept as minimum as possible. Overall dimension, weight, proposed fixing arrangement etc. shall be indicated in the offer																																
	Chapter 3 - System Configuration																																	
3.1	Muilti-way SP Telephone: SPT shall be COTS type suitable for marine applications. Muliti-way SPTs of 12,24 extensions shall be supplied along with noise cancelling handset. It shall be provided means to select one of the various positions with which the user may need to communicate in a single functional line through selector switch.																																	

	HINDUSTAN SHIPYARD LIMITED (A Govt. of India Undertaking) Ministry of Defence Gandhigram, Visakhapatnam - 530005	Electrical Design	REV: 001
		Yard No: 11190-91	DATE: 26.08.2020
		SPT	Page 7 of 25

3.2	Junction Box: COTS type Junction Boxes suitable for marine use shall be used for interfacing the SP Telephones within a functional line. JB terminals, dimensions, connection for a single functional line within the JB etc. shall be indicated in the offer.	
3.3	Headset: The headset with integral noise cancelling microphone shall be used in acoustically harsh environments or where hands-free operation is required (i.e. Noisy areas and weather deck). Stowage clips are to be provided near the SP Telephone sets.	
3.4	Flasher Hooter and relay Box: SP Telephones shall have provision for suitable audio-visual indications to annunciate incoming call at noisy locations by means of an audible bell and a visual indication. Relay box shall be used to connect the flasher hooter to the SP telephone.	
3.5	Directory Plates: Directory plates must be provided alongside each telephone unit. Diagram plate indicating connection details shall be affixed on the equipment directory shall be in aluminium anodised plate.	
	Chapter 4 - Scope of Supply	
4.1	As mentioned the system functionality, the types of groups and the number of positions for each group, firm shall supply the required units and subunits to ensure the system functionality. Complete list of items shall be submitted with offer. Refer SPT Single Line Diagram enclosed at Annexure-3 for Bill of Material.	
	Chapter 5 - Technical Requirement	
5.1	Power supply: Ship's power supply of 230V AC, 1Ph, 50Hz shall be made available to the relay box flasher hooter unit. The SPT system shall have a provision for connecting to ship's 24V DC supply, thus operating as a conventional telephone system without the use of hand cranking.	
5.2	Internal wiring: Internal wiring of the equipment shall use LHF wires.	
5.3	Cable: System Cables are excluded from firm's scope of supply. Any other special cables required shall be supplied by the firm. Shipyard will indicate Cable part no and OD post placement of order. Inter unit cable diagram (Line diagram) specifying type of cable used to be provided by the firm along with the Binding Data.	
5.4	Cable Entry Glands: Cable entry glands shall conform to specification BS6121/ EN 624440-2013 for incoming and outgoing cables. Cable glands shall be fitted with the equipment, the gland size shall be suitable to the OD of the cable indicated by the Shipyard.	
5.5	Terminal: Bolted type/WAGO type terminal & crimped socket of electrolytic copper shall be provided for all incoming and outgoing cables. Adequate spare terminal strip shall be provided for provision of additional control and indication facilities. Adequate space shall be provided inside	

	HINDUSTAN SHIPYARD LIMITED (A Govt. of India Undertaking) Ministry of Defence Gandhigram, Visakhapatnam - 530005	Electrical Design	REV: 001
		Yard No: 11190-91	DATE: 26.08.2020
		SPT	Page 8 of 25

	the equipment for bending and termination of incoming & outgoing cables.	
5.6	Earth Terminals: An external earth terminal of brass or stainless steel is to be provided for devices and control panel.	
5.7	Installation Material: One set of installation material per ship inclusive of special tools if any, special cables if any, plugs, adapters, mating flanges, sockets (with accessories), pins and cable lugs, vibration mounts etc. as required for satisfactory completion of system installation on board ship shall be supplied.	
5.8	Components: All components shall be of Naval (Marine) approved type. Standard specification and grade of material of each component used shall be indicated in the binding drawings. Make and type of components are to be listed in the binding drawings. Indication lamps used shall be of LED type. The equipment shall be designed so that all components may be removed from the front of the cubicles with the front cover only removed. There shall be no hidden connection. All the components of the equipment shall have easy access for removal/ refit.	
5.9	Enclosure: The enclosure shall be aluminium/steel/alloy/composite materials having suitable arrangement for flush/bulkhead mounting type installation on-board the ship. Subunits shall conform to Ingress Protection IEC 60529 viz. IP22 for indoor units, IP44 for machinery compartments and IP56 for outdoor units as detailed at Annexure-1. The enclosure protection for the equipment shall be indicated in offer.	
5.10	Lifting Arrangement: Equipment weighing more than 40 Kg shall be provided with collar eyebolts or suitable lifting lugs/arrangements. If the eyebolts cannot remain in site after the equipment has been installed in the ship, provision shall be made for their securing arrangement on the equipment.	
5.11	Painting: Enclosure finish colour shall be admiralty grey, semi-gloss as per approved painting specifications/procedures. Painting shall conform DGS 251/RAL 7001	
5.12	Talley and diagram Plates: Tallies and diagram plates for all equipment shall be made of anodized aluminium alloy/SS. Size of tally plate and their letters shall conform to specification NES-723. 230V danger tally shall be provided on the equipment at a permanent place where required. Safety markings on main equipment and associated devices/units shall conform to NES 784.	
5.13	EMI/EMC Standard: The equipment shall be capable of operating in the vicinity of other equipment / systems without causing or responding to undesirable electro-magnetic energy. The equipment design shall consider electromagnetic interference (EMI) coming from the external sources, generated from within its own enclosure and degrading the performance of the equipment. EMI may be reduced by judicious	

	HINDUSTAN SHIPYARD LIMITED (A Govt. of India Undertaking) Ministry of Defence Gandhigram, Visakhapatnam - 530005	Electrical Design	REV: 001
		Yard No: 11190-91	DATE: 26.08.2020
		SPT	Page 9 of 25

	selection of components and use of good engineering practices like grounding, bonding and shielding. a) COTS equipment shall comply IEC 60945/IEC 60533 or equivalent EM standards. b) All equipment shall have the provision of grounding, bonding and shielding as per NECP 500 and MIL-STD-1310H.	
5.14	Permissible Temperature Rise: The equipment must be designed so that the maximum permissible operating temperature of components is not exceeded during normal operating conditions in a maximum ambient temperature as specified in this specification.	
5.15	Cooling: Experience in onboard use indicates a significant proportion of static conversion equipment failures occur as a result of overheating. Sufficient cooling arrangements by natural air convection shall be provided in the equipment in order to meet the permissible limit of temperature rise.	
5.16	Reliability and Maintainability (R&M): (a) Mean Time Between failure (MTBF): The design of the equipment shall be such that the estimated mean time interval between failures shall be greater than 10000 hours. (b) Self Noise & vibration: Care is to be taken in the design and manufacture to ensure that the air borne noise and structure borne vibrations produced by the units/ devices, the self-induced air borne noise and vibration level shall meet ships stealth features. (c) Mean time to Repair (MTTR): System shall be designed for low MTTR not exceeding 15min.	
5.17	Control and Protection: The following protection principle shall apply to electrical and electronic equipment: a) Internal fault protection is to : (i) Prevent further damage within the equipment, subsequent to a fault (ii) Prevent damage to the converted power loads (iii) Prevent the primary supply going out of specification. b) External fault protection is to: (i) Prevent damage to the equipment, subsequent to a fault external to the equipment. (ii) Where Practicable, include current limiting techniques to allow the equipment to work with a short circuit onto the output. (iii) Be defined in terms of conditions under which the equipment shall trip. c) Estimated and calculation of the effects of fault conditions are	

	HINDUSTAN SHIPYARD LIMITED (A Govt. of India Undertaking) Ministry of Defence Gandhigram, Visakhapatnam - 530005	Electrical Design	REV: 001
		Yard No: 11190-91	DATE: 26.08.2020
		SPT	Page 10 of 25

	include: (i) Stored energy in the load (e.g. resulting from shunt capacitors motor loads) (ii) Stored energy in the equipment itself (e.g. in Back-up Batteries) d) The design of protective arrangements shall take into account thermal capacity of the components being protected and heat sink arrangements incorporated within equipment. The contribution to R&M figures of protective arrangements must be considered.	
5.18	ESD Protection: The system design shall take into account adequate measures for Electro Static Discharge (ESD) control and protection at PCB/ module/ assembly and unit level. Each Electro Static Discharge sensitive part/assembly shall be duly marked with a symbol/ warning. The firm shall use ESD protective materials for handling, packaging storage and transport.	
5.19	Environmental Stress Screening (ESS) Test: ESS test for electronic components/sub-systems is required to be carried out for 100% components/ parts/ assemblies as per IHQMOD(N) Policy letter 66301/Policy-07/DQA(N)/QA-07 dt 09 Aug 16	
5.20	The offered SPT system shall comply with EED-50-08 (R2). Alternatively the SPT shall be supplied with Class type approval certificate confirming to IEC Standards.	
5.21	Shock / vibration test details to be indicated in the technical offer	
5.22	Humidity and heat run tests to comply with IEC 61347-1.	
	Chapter 6 – General	
6.1	Ship's Data: The System shall be suitable for fitment on DSV class of ship with the following features:- a) Length Overall - 119.40m b) Length Between Perpendiculars – 110.70m c) Breath MLD – 22.80m d) Depth to Deck10 – 10.40m e) Design Draft – 6.00m f) Total compliment - 215	

	HINDUSTAN SHIPYARD LIMITED (A Govt. of India Undertaking) Ministry of Defence Gandhigram, Visakhapatnam - 530005	Electrical Design	REV: 001
		Yard No: 11190-91	DATE: 26.08.2020
		SPT	Page 11 of 25

6.2	Classification Society: Vessel Shall be designed, built and outfitted as per applicable provisions and regulations as given in the Naval Rules of Indian Register of Shipping. The Class Notation for the Diving Support Vessel as follows. Swastika SUL "Diving Support Vessel", FDA, VIB(HGL), HELIDK, RAS(AB) Swastika IY, DP(2), EP, DSV Descriptive Note: "Submarine Rescue vessel", "Deck strengthened for 5t/m²", Special Government Service".	
6.3	Operating Condition: The system devices/equipment shall operate satisfactory in the marine environmental (coastal conditions) and other operating conditions enumerated in the succeeding paragraphs.	
6.3.1	Seaway conditions: a. Roll : Max 20° with 10 sec period. b. Trim : Max 5° c. List : Max 20° from vertical. Pitch : Max 6° with 20 sec period.	
6.3.2	Sea Worthiness: Main equipment along with its control equipment & accessories should meet sea worthiness criteria as mentioned below. The sea worthiness of the ship shall be as follows:- a. Sea worthy for transit on all headings upto Sea State 7 and survivable on best headings at Sea State 8. b. Capable of operating Helicopter in Sea State 6 on best heading. c. Capable of conducting Diving Operations upto Sea State 4. d. Capable of Dynamic Positioning operations upto Sea State 4.	
6.3.3	Units and Language: Language shall be English. Metric Units shall be used.	
6.3.4	Environment Condition: The equipment and the accessories including all integral and associated service system should be capable of continuous operation when the ship is in the following conditions: a. Ambient Conditions : b. Sea water temp : 1 deg.C to + 35 deg.C c. Max relative humidity : 100% at 38 deg C d. Salinity of water : upto 35 ppt Max. Machinery room temp: Machinery room compartments maintained at ambient (33⁰C) + 5 in open condition and between 45 to 55⁰C in closed condition.	

	HINDUSTAN SHIPYARD LIMITED (A Govt. of India Undertaking) Ministry of Defence Gandhigram, Visakhapatnam - 530005	Electrical Design	REV: 001
		Yard No: 11190-91	DATE: 26.08.2020
		SPT	Page 12 of 25

6.4	Commonality: The firm to mention the level of commonality achieved within the system at the following levels :- (a) Module/Sub- module level (b) PCB level (c) Component level	
6.5	Weight Data Sheet: The firm to furnish Weight data sheet for Equipment detailing the following for the use of calculation for weight curve :- (a) Carcass weight (b) Total weight of equipment (c) Centre of gravity showing 3 axis coordinate	
6.6	Security: The information about the ship and the requirements mentioned in the SOTR are not to be communicated to any third party without prior approval of IHQMOD(N).	
6.7	Warranty: The Equipment with Associated controls/ instrumentation shall be guaranteed for stipulated performance for a time period mentioned as per STAC/Commercial Clause. The equipment supplied shall be warranted from defects arising due to the manufacturer/firm and performance for the said period and cover all the defects arising from malfunction through design faults, inappropriate material, bad production and non-conformance to specifications. Any expense on account of repair/ supply of spares against guarantee defects shall be borne by the firm.	
6.7.1	Extension of warranty: Firm shall mandatorily indicate in the offer, the annual rate for extended warranty period, in the event of expiry of warranty period as detailed above along with the associated commercial terms and conditions if any.	
6.8	Upgrades and Obsolescence / Product Support: Latest version of the equipment/ system at the time of tendering shall be provided. All upgrades and modifications thereafter in the hardware and software of the system need to be communicated to the Navy for the complete support life of 25 years from the date of commissioning of the equipment on board ship excluding electronic item for which the period is 10 years. Obsolescence of subsystem, components, parts and assemblies need to be communicated to Navy at least two year in advance with recommended remedial action. A maintenance contract may be offered for consideration and negotiation at the later date. Firms supplying imported equipment/systems are to ensure that product support and aftersales service in India are available for all assemblies/ modules/ software including third party supplies prior commencement of trials.	

	HINDUSTAN SHIPYARD LIMITED (A Govt. of India Undertaking) Ministry of Defence Gandhigram, Visakhapatnam - 530005	Electrical Design	REV: 001
		Yard No: 11190-91	DATE: 26.08.2020
		SPT	Page 13 of 25

6.9	Safety standards: Equipment shall offer total safety to personnel from moving parts and other associated equipment from vibrations. Safety standards as per MIL STO 454/ equivalent shall be met.	
	Chapter 7 - Spares, Tools and Test Equipment	
7.1	Onboard Spares : OEM recommended onboard spares for schedule servicing, maintenance & break down maintenance falling due within the first operation cycle for 02 years shall be provided for the equipment in ILMS Ver 2 format (Integrated Logistics Management System) indicating the item code number, quantity and item wise cost. The Spares consumed within the guarantee period to rectify / liquidated known defects shall be replaced free of cost. The supplier shall prepare the list of OBS (including onboard maintenance tools) based on the Reliability and Maintainability data and taking into account IN's maintenance philosophy, and shall forward to IHQ MOD (Navy) for vetting. The complete inventory of system parts including OBS & B&D spares is to be provided in INCAT (Indian Naval Catalogue of Inventory) compatible format in electronic media for ILMS (Integrated Logistics Management system) of Indian Navy, for the management of spares. The supplier shall provide both hard copy as well as soft copy. Refer Annexure-1	
7.2	Five Year Base and Depot (B&D) Spares. Base spares recommendation shall cover maintenance / overhaul requirements of 5 years including two refits shall be provided for the equipment in ILMS Ver 2 format. Recommendations for insurance holding of long lead items are also to be indicated. Itemized cost of B&D spares are to be forwarded with the main offer along with part identification list of spares. The list would contain price, description, Pattern no. and quantity fitted on each equipment in respect of various parts / components. The quotation of spares shall be valid for at least 18 months. The Buyer shall subsequently range and scale the B&D spares. The cost negotiation of B&D spares would be carried out by a committee constituted by the Buyer, wherein the seller's and sub-vendor's representative would be a member. The OEM shall undertake procurement of the ranged and scaled spares as per the ordering instructions issued by the IHQ MoD (N). Refer Annexure-1.	
7.3	Installation & Commissioning Spares: The supplier's service of engineer shall supply/ carry one set of installation and commissioning spares along with the main equipment.	

	HINDUSTAN SHIPYARD LIMITED (A Govt. of India Undertaking) Ministry of Defence Gandhigram, Visakhapatnam - 530005	Electrical Design	REV: 001
		Yard No: 11190-91	DATE: 26.08.2020
		SPT	Page 14 of 25

	Chapter 8 - Binding Data , Design Drawing & Technical Documentation	
8.1	Binding Drawing: The firm shall submit approved and as made drawings sufficiently detailed to show the manner of construction and operation, the method of assembling and dismantling. The following binding drawing/documents in duplicate (both hardcopy & softcopy) shall be submitted to IRS for approval with a copy to shipyard within 4-6 weeks after placement of the order. (a) Installation drawings indicating overall dimensions, C.G., weight, maintenance envelope, IP rating, power ratings, vibration mount details etc of each unit. Detailed foundation drawing including bolting plan shall be included. (b) Mounting arrangement drawings with installation instructions. (c) Heat Dissipation of individual units in compartment & in close loop ventilation system, as required for the system. Other interface requirement from ship viz. air, water, cooling etc to be indicated. (d) Material list Indicating Part No., Quantity, Material, Makers name etc. (e) Block diagram of all major assemblies showing interconnection between these assemblies as well as cables specifications. (f) Power supply scheme for the system with specific mention of UPS requirement. (g) Cable length limitation etc, if any. (h) Recommended arrangement of devices in nominated compartments. (i) Circuit diagram, wiring diagrams, wiring schedules, terminal connection and core connection details. (j) Details of standard and optional factory tests	
8.2	Design Documents/Drawings: All associated design documentation, drawings and equipment list applicable must be in English language. All drawings and documents shall contain dimensions and other parameters in metric units (SI Units). The drawing and documentation shall be complete to enable installation on board. These shall cover all subassemblies and accessories of the equipment. The documents/drawings shall be provided in both hard copy form and on CD_ROM. An Interactive Electronic technical Manual in IETM level 4 format also needs to be provided with the system. Following draft documents shall be presented for approval of IHQMOD(N): a) Technical and operation Instruction Manual b) Onboard Maintenance Manual	

	HINDUSTAN SHIPYARD LIMITED (A Govt. of India Undertaking) Ministry of Defence Gandhigram, Visakhapatnam - 530005	Electrical Design	REV: 001
		Yard No: 11190-91	DATE: 26.08.2020
		SPT	Page 15 of 25

	c) field and Depot Maintenance manual d) Operation Maintenance document e) Installation and testing specifications/manual f) Certified Test Data and report g) Parts and Tools Catalogue h) Installation drawings in reduced Size i) As Fitted Drawings j) Any Other Special Instructions for Installation and Preservation k) Conformation of Standards Specified l) Test Procedures and Documentation m) Heat Dissipation of Devices n) Storage, handling, transportation details etc. o) Details upto 2nd level maintenance for repair and troubleshooting. Component level maintenance details to be provided along with list of components. p) The software in the system shall comply with any of the established standards like MIL-498, IEEE 12207 etc. All Documents as per the standards related to software design, setting and maintenance shall be provided.	
8.3	Technical Documentation: Details of technical documentations to be supplied are as mentioned below: Separate manuals in respect of following for both equipment and system shall be provided in hard and IETM level 4 format:- Refer Annexure-2 (a) Operation and Specifications including onboard Repair and Maintenance. This should include information about the equipment (such as serial number, trial reports, etc) and the manufacturer (such as addresses, telephone and fax numbers, email, etc). (b) Repair Technical Document with detailed drawings (c) Complete Parts List	

	HINDUSTAN SHIPYARD LIMITED (A Govt. of India Undertaking) Ministry of Defence Gandhigram, Visakhapatnam - 530005	Electrical Design	REV: 001
		Yard No: 11190-91	DATE: 26.08.2020
		SPT	Page 16 of 25

	S.No	Description	No. of Copies		
	1	User Handbook (Including Technical Description, operation Instruction and Service log Book)	Two sets of documents shall be supplied in CD_ROM in addition to two hard copies for each ship.		
	2	Technical Manual including Setting to work & test Procedures.			
	3	CPIL/PIL			
	4	Servicing and Maintenance Manual (field and depot)			
	5	Unpacking and Installation specifications/ drawings			
	6	Recommended list of OB spares, testing tuning spares, tools and test jigs.			
	7	Installation checks, HAT/SAT schedules			
	8	As made drawings including winding & performance data			
	9	Test certificates			
	Chapter 9 - Quality Assurance				
9.1	The detail design, material and workmanship shall be in accordance with the best worldwide recognized marine practices, to ensure reliability, durability and ease of maintenance which comply with the ship's requirements. The design shall be such that weight and size are reduced to the minimum practicable, ensuring no compromise in reliability or significant design criteria. A Quality Assurance Program shall be specified by the firm in this offer.				
9.2	Quality Assurance Program:				
9.2.1	Details of test equipment, test methods, preliminary qualification tests, etc shall be indicated. All tests shall be carried out by firm at his own works, in presence of and inspecting authority, prior to dispatching the equipment to the customer.				

	HINDUSTAN SHIPYARD LIMITED (A Govt. of India Undertaking) Ministry of Defence Gandhigram, Visakhapatnam - 530005	Electrical Design	REV: 001
		Yard No: 11190-91	DATE: 26.08.2020
		SPT	Page 17 of 25

9.2.2	Quality assurance plan proposed and any subsequent amendment shall be discussed and agreed upon between IRS & the firm prior to placement of order.	
	Chapter 10 - Inspection & Testing	
10.1	Inspection: (a) For Design : Directorate of Naval Design (SSG) / Directorate of Electrical Equipment (DEE) of Indian Navy (b) For Installation : Warship Overseeing Team (WOT) of IN at HSL, Vizag (c) For ship trials : IRS (d) For QC : IRS (e) For approval of HATs/SATs schedule: IRS	
10.1.1	The product offered by the firm shall conform to standard engineering practices. The equipment shall be subject to stage inspection and final test and trials by IRS. Any deviation from the mentioned specifications shall have to be brought to the notice of IHQMOD(N).	
10.2	FATs: FAT for the first system shall be carried out at OEM premises by the reps of classification society including QA representative against ATP mutually agreed by IRS and OEM. During FATs firm would demonstrate system shall meet the functional and performance requirements indicated as per approved SOTR. Firm shall submit FAT document to IRS within 03 months after placement of order for approval. The FATs procedure shall comprise of: (a) Functional test (b) Verification of design, especially firmware and software (c) Test equipment used, calibration requirements. (d) Pass / Fail Criteria. (e) Expected duration and time phasing	
10.2.1	One copy of FAT report shall be submitted to IHQMOD(N) and shipyard for record/ comments.	
10.3	HATs/SATs: HAT/SAT Schedule shall be prepared by firm and forwarded to IRS for Approval within 06 months of Purchase order issued to firm.	

	HINDUSTAN SHIPYARD LIMITED (A Govt. of India Undertaking) Ministry of Defence Gandhigram, Visakhapatnam - 530005	Electrical Design	REV: 001
		Yard No: 11190-91	DATE: 26.08.2020
		SPT	Page 18 of 25

10.4	Service of Engineers: The firm shall provide the necessary service of engineer to carry out the following activities: a) Setting to work b) Harbor and Sea Trials	
10.4.1	Firm shall depute firm's experienced, qualified and expert engineer/technician to carry out the above activities onboard in-line with ship's construction timeline for the system. Above activities shall be undertaken to ensure satisfactory performance of the system onboard and for proving the system to the inspection agencies as per approved test procedure.	
10.4.2	The firm shall indicate total cost (in price bid) for executing all technical activities in the offer. No extra man-days/ payment on this account shall be admissible. Activity-wise cost break up shall also be mentioned in the price bid for reference.	
10.5	System Performance responsibility: The firm shall present the system for performance Evaluation Trials (HAT/SAT) to prove the expected performance assured. In case of any irregularities in the operation/ performance of the system or non-conformance to specified parameters observed on integration with ships system, the firm is bound to rectify the defect. The firm shall ensure complete responsibility of satisfactory operation of the system on board.	
	Chapter 11 - Other terms and Conditions	
11.1	Shipping: All equipment shall be adequately packed and protected with supports to ensure adequate protection during all modes of transportation. Each unit within a package/container shall be clearly marked for identification. The container shall clearly indicate the item description with caution marks, quantity, weight, size, etc. A separate document giving complete details and instructions for storage, preservation, handling and transportation after delivery shall be supplied, The firm shall indicate the delivery schedule, port of embarkation, transport, packing, preservation, insurance, etc.	
11.2	Training: The OEM shall conduct an operational and maintenance training course at the shipyard premises to the ship's crew / maintainers. Complete training package for on board exploitation, maintenance and for second level maintenance along with tools and test kit to be offered. The level and number of personnel recommended for training also needs to be indicated and shall be decided during TNC. All training material shall thereafter be handed over to Navy for future training requirements, The training schedule shall be prepared in consultation with WOT/Ship Staff well in advance.	

	HINDUSTAN SHIPYARD LIMITED (A Govt. of India Undertaking) Ministry of Defence Gandhigram, Visakhapatnam - 530005	Electrical Design	REV: 001
		Yard No: 11190-91	DATE: 26.08.2020
		SPT	Page 19 of 25

11.3	Price: Quoted price shall include itemized price list of major components of the equipment, activities related to design work and other activities included in the scope such as services of engineers as required for installations, testing, commissioning & training etc.	
11.4	Validity of Offer: The Offer from the firm must be valid for a minimum period of 6 Months. The Lead-time necessary for supply of hard and software along with the term of payment may also be included in offer.	
11.5	License: If the equipment is manufactured under license in collaboration in India, the firm is to indicate the following:- (a) Collaboration agreement already signed or not (b) Name and address of the collaborator/principal and details of registration license (c) The extent of indigenous manufacture of components, transfer of technology and collaboration for supply and support of equipment including those supplied directly by the collaborator (d) The yearly production capacity of the Indian licenses	
11.6	Scope of Offer: The following information shall be supplied with the initial offer: (a) Outline drawings of the equipment indicating overall dimensions, weight, CG and maintenance envelope. (b) Power supply requirements with load (c) Heat dissipation of the main equipment, devices and sub-units (d) Details of other ship services required (e) Tools required for installation and maintenance (f) Recommended on board and base spares holding (for 2 years and 5 years operation respectively) (g) Special tool and test equipment to be supplied for on board maintenance and 3rd and 4th level maintenance (h) Manufacturer's list of spares for installation (i) Delivery time from receipt of order (j) Trial and commissioning time for complete system on board	

	HINDUSTAN SHIPYARD LIMITED (A Govt. of India Undertaking) Ministry of Defence Gandhigram, Visakhapatnam - 530005	Electrical Design	REV: 001
		Yard No: 11190-91	DATE: 26.08.2020
		SPT	Page 20 of 25

	(k) Part identification list at sub units level (l) List of main equipment included in the standard scope of supply (m) List of accessories included/ not included in the standard scope of supply (n) List of optional units and accessories not included in the standard scope of supply (o) List of equipment required for installation and operation of the equipment and not supplied by the firm (p) Clause wise Compliance matrix for the SOR (q) Terms of Payment	
11.7	Sufficiency Clause: All deliverables supplied with the equipment shall be sufficient for satisfactory operation of the system. If any additional item is thereafter required for satisfactory operation of the system as described in the tender, the same shall be supplied by the firm with no cost implication.	
11.8	The cable laying shall be carried out by HSL and the connectorization, STW, HATs and SATs are in Supplier's scope.	
11.9	Preservation, Packaging and Shipping: The stores (including OBS and B&D Spares) shall be supplied in long-term preserved condition that is suitable for storage under tropical high humidity conditions for a period of 24 months.	

[cont.....]

							Equipm ent BQM	Equipm ent BQM	Equipment BQM	Equipment BQM	Equipment BQM	Equipment BQM	Equipment BQM	Equipment BQM	Equipment BQM	Equipment BQM	Equipme nt BQM
Material Master	Materi al Master	Material Master	Material Master	Materi al Master	Mate rial Mast er	Mat eria l Ma ster	Material BQM	Material BQM	Material BQM	Material BQM	Material BQM	Material BQM	Material BQM				
22	23	24	25	26	27	28	29	30	31	32	33	34	35	36	37	38	39
OEM	OEM	OEM	OEM	OEM	OEM	OE M	OEM	OEM	OEM	OEM	OEM	OEM	OEM	OEM	OEM	OEM	OEM
Manufac turer Name	Auth Suppli er Name	Specific ation	Charact erstics	Drawin g Refere nce	PIL Refe renc e	Uni t Wei ght	EEquipm ent	A- Assemb ly	S- SubAssemb ly	L-Stockable	KIT	Superior Element	PIL Qty	OBSQty	B&Dqty	LTE qty	MRLSQt y (Ranging &scaling)
Manufac turer Details (Name) for item other than an Eqpt (in case different from OEM of Main Eqpt)	Supple r Details (Name of auth supplie r) for Eqpt/a ssy Sub- assy/S tockabl e/Kit in case differe nt from OEM	Specifia ction (Any standar d Spec or Material Spec which)f or the item	Contane d the propertie s/charac teristics of the correspo nding item viz dimensio n etc.	Drawin g Refere nce	PIL Refe renc e (PIL No. Versi on Pag e and Line no.)h t	Uni t Wei g.	If item Code is a main Equipm ent then type Y,else leave the ce;; blank.	1. If item is an Assemb ly,then type Y else N 2.If value is 'Y' then fill up column Named "Superio r Element with corresp onding Equipm ent Code.	1.If item Code is an SubAssemb ly then typ r Y,else type N. 2.If value is 'Y' then fill up column Named 'Superior Element with correspon ding Assembly identification no.orth e Equipment identification no.in cas xe item is not part of any Assembly.	1.If item Code is a Spare partthen type Y,else type N. 2.If value is 'Y' then fill up clumn Named 'Superior Element with correspon ding Sub- Assembly identification no.or Assembly identification no.of Assembly identification no.or the Equipment Code (in case item is not part of any sub- assembly or Assembly).	1.If itemCode is a KIT,then type Y,else leave the cell blank. 2.If value is Y,then fill up column named 'Superior Element with corresponding Equipment Code. 3.List of Constituent part no. and Qty comprising the kiy is to be forwarded as separate sheet for each list Refer Annexure 'A'	Indicates the higher linked Sub- Assembly or Assembly or Main Equipmento which the itemcode belongs	Enter the PIL quantity of material which is mentioned column item Code,Qua ntity of item fitted in particular equipment	Enter the OBS quantity of material which is mentioned in column item Code	Enter the B&D quantity of material which is mentioned in column item Code	Enter the LTE quantity of material which is mentioned in column item Code	Qty indicated in Manufact urer recomme nded List of spares for the item in column item Code
CHAR(2	CHAR(	CHAR(	CHAR(2	CHAR	CHA	CH	CHAR(1	CHAR(1	CHAR(1)	CHAR(1)	CHAR(1)	CHAR(40)	NUM(18,0)	NUM(18,0)	NUM(18,0)	NUM(18,0)	NUM(18,

	HINDUSTAN SHIPYARD LIMITED (A Govt. of India Undertaking) Ministry of Defence Gandhigram, Visakhapatnam - 530005	Electrical Design	REV: 001
		Yard No: 11190-91	DATE: 26.08.2020
		SPT	Page 23 of 25

55)	255)	255)	55)	(255)	R(25 5)	AR(8)	)	)									0)

Note: All data are entered just for examination.

VED – VITAL/ESSENTIAL/DESIRABLE analysis of spares to be carried out by OEM prior to submission to the BUYER.

Notes: -

Data regarding maintenance spares/stores like lubricants, sealing compound, gases should be given separately giving source of supply.

Data furnished as OBS and B&D should also include software backups, as applicable.

In 'Remarks' column following information (if applicable) be given: -

If an item has a shelf/operational life it be marked as 'G' and life indicated.

Matching set of components be indicated.

Item which can be locally manufactured should be marked 'LM'

Items which cannot be manufactured in India due to sophisticated design/technology may be marked as 'SI' (Special item).

If a component/assembly is common to other similar equipment offered by the OEM earlier, these should be marked 'CM' and name of the equipment be indicated.

OBS and B&D spares list should be drawn out of the 'Part list' of the equipment, which should be separately given as part of Technical Manuals.

If the main equipment consists of other, then OBS and B&D spares list should be prepared for them under proper heads. OBS and B&D spares list is to be per the maintenance concept of the customer.

Items provided along with the equipment as spares should be included in OBS and B&D list.

Modules/Shop Replaceable Unit (SRU)/ assemblies should be listed and their components should be listed components should be included under them so as to relate each item of spare to their module/SRU/ assembly.

OBS and B&D list for test equipment should also be provided on the similar format.

Buyer would also have the option to amend the MRL-OBS proposed by the bidder during the Technical Negotiation of individual equipment to ensure its sufficiency, based on its past experience of exploitation of same/similar equipment.

Cost to be indicated in Price bid only.

Sufficiency clause: - the seller would either 'Buy Back' the spares rendered surplus or exchanges them on cost to cost basis with the spares as required by the Buyer. The said spares would be purchased or replaced by the seller, based on the prices negotiated in the contract.

	HINDUSTAN SHIPYARD LIMITED (A Govt. of India Undertaking) Ministry of Defence Gandhigram, Visakhapatnam - 530005	Electrical Design	REV: 001
		Yard No: 11190-91	DATE: 26.08.2020
		SPT	Page 24 of 25

Annexure-2

TECHNICAL DOCUMENTATION
(To be filled by OEM)

Name of Vessel/Equipment: _____

Original Equipment Manufacturer (OEM): _____

S.No	Technical Literature	Unit Cost	Scale For 02 Vessels	Total Cost	Remarks
1.	User Handbook/Operator's Manual				
2.	Design Specifications				
3.	<u>Technical Manual</u> (a) Part I Tech description, specifications, functioning of various Systems. (b) Part II Inspection /Maintenance tasks Repair procedures, materials Tools (SMT's)/ Special Test Eqpt (STE)s (c) Part III Procedure assembly/disassembly, repair up to component level, safety precautions. (d) Part IV (i) Part list with drawing reference (ii) List of SMT/STEs with Test Bench				
4.	Manufacturer's Recommended List of Spares (MRLS)				
5.	Illustrated Spare Part list(ISPL)				
6.	Technical Manual on STE with drawing reference.				
7.	Soft copy on the above Tech literature				
8.	Any other (specify)e.g. Service logs etc.				

Total Cost

- Notes: -
1. In case any additional equipment is used, their tech literature will be included.
 2. If certain technical literature is being provided free of cost, it should be indicated in the remarks column.
 3. Cost to be indicated in Price Bid Only.

	HINDUSTAN SHIPYARD LIMITED (A Govt. of India Undertaking) Ministry of Defence Gandhigram, Visakhapatnam - 530005	Electrical Design	REV: 001
		Yard No: 11190-91	DATE: 26.08.2020
		SPT	Page 25 of 25

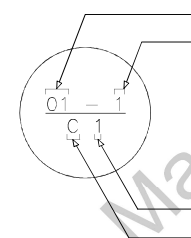
DISTRIBUTION OF DOCUMENTS

S.No	DISTRIBUTION OF DOCUMENTS	TYPE OF DOCUMENTS	No. OF COPIES	Vendor COMPLIANCE (Y/N)
1.	FAT PROTOCOLS FOR OWNERS APPROVAL	CD	2	
		PRINT	5	
2.	GRAQ PROTOCOLS FOR OWNERS APPROVAL	CD	2	
		PRINT	5	
3.	SCHEMATIC SYSTEM DRAWINGS	CD	2	
		PRINT	9	
4.	AS MADE EQPT. DRAWINGS	CD	2	
		PRINT	10	
5.	CPL/PIL	PRINT	8	
6.	EQPT HAND BOOK TECH.OPERATION MANUAL	CD	2	
		PRINT	10	
7.	INSTALLATION SPECIFICATION MANUAL	CD	2	
		PRINT	10	
8.	EQPT.FIT BOOK	CD	1	
		PRINT	7	
9.	TEST CERTIFCIATES	CD	3	
		PRINT	7	
10.	TRIAL REPORTS-FAT,HAT&SAT	CD	2	
		PRINT	7	
11.	MATERIAL SCHEDULE	PRINT	6	
12.	MAINTENANCE SCHEDULE	PRINT	10	

"This drawing is schematic only"

Legends:

1. Component Number



Deck No.
Symbol No.

SERIES

GROUP CODE A or C or E or M or H or DI or D

2. Group Coding

- A — Anchoring Sound Power Telephone Group
- C — Conning and Steering Sound Power Telephone Group
- E — Electrical & Communication Sound Power Telephone Group
- M — Machinery Sound Power Telephone Group
- H — Helo & AVCAT Sound Power Telephone Group
- DI — Diving & DP Sound Power Telephone Group
- D — Damage Control Sound Power Telephone Group

Notes:

1. The exact position can be finalized upon receipt of equipment OEM details.

Class Notations:

~~IRS: 5SUL "Diving Support Vessel", FDA, VIB(HGL), HELIDK, RAS(AB)~~

~~5IY, DP(2), EP, DSV~~

~~Descriptive Note: "Submarine Rescue vessel",~~

~~"Deck strengthened for 5t/m²", Special Government Service".~~








REV	DESCRIPTION		DATE	SIGN
DRAWN	PL	CLIENT	INDIAN NAVY	VIK-SANDVIK  DESIGN INDIA PVT. LTD. CHENNAI 10/14, 8TH STREET GOPALAPURAM, CHENNAI 88 +91 44 4297 2000 FAX +91 44 4297 2022
CHECKED	JON	SHIP	DIVING SUPPORT VESSEL	
APPROVED	MOU	DATE	02-01-2020	
		CLASS	IRS	
<u>HINDUSTAN SHIPYARD LTD.</u> VISAKHAPATNAM. INDIA.			<u>SCALE</u> NTS, A3	<u>SHIP No.</u> VC11190&VC11191
	TITLE : SLD OF SOUND POWERED TELEPHONE		<u>DRAWING No.</u> 80302 Rev 0	
			SHEET No. 01 OF 14	

ALL RIGHTS RESERVED











This drawing is the property of VIK-SANDVIK Design India (P) Ltd., and it must not be copied or imparted to any unauthorized third party.

8	7	6	5	4	3	2	1
A							
B							
C							
D							
E							
F							

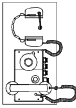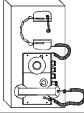Eqpt. No.	Symbol	DESCRIPTION	OEM	EQPT. PATT. NO	SHEET NO.3 Qty.	SHEET NO.4 Qty.	SHEET NO.5 Qty.	SHEET NO.6 Qty.	SHEET NO.7 QTY	SHEET NO.8 QTY	SHEET NO.9 QTY	SHEET NO.10 QTY	SHEET NO.11 QTY	SHEET NO.12 QTY	SHEET NO.13 QTY	SHEET NO.14 QTY	TOTAL Qty.
1		NWT IP22 SOUND POWER TELEPHONE	---		1	3	1	3	5	2	---	5	10	3	6	1	40
2		WT IP 44 SOUND POWER TELEPHONE WITH HEADSET	---		---	4	---	1	6	4	4	---	---	1	---	---	20
3		OUTDOOR IP56 SOUND POWER TELEPHONE WITH HEADSET	---		1	4	---	1	---	---	---	1	---	---	---	---	7
4		FLASHER, HOOTER AND RELAY BOX	---		---	---	---	---	---	3	4	---	---	1	---	---	8
5		NWT IP22 SOUND POWER TELEPHONE WITHAMPLIFIER			1	1	---	1	---	1	---	1	1	---	1	---	7
6																	
7																	
8																	

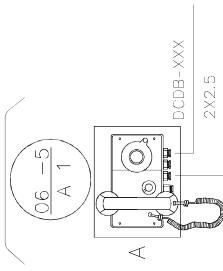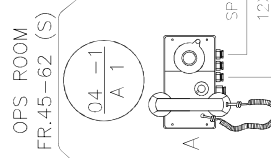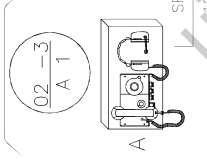
								1	2	3	4	5	6	7	8
A - Anchoring Sound Power Telephone Group								TOP OF DK-06							
A	WHEEL HOUSE FWD FR.32-64							A							
								A							
B	OPS ROOM FR.45-62 (S)							B							
								B							
C	FOXLE, FWD BHD FR.18							C							
								C							
D								D							
								D							
E								E							
								E							
F								F							
								F							

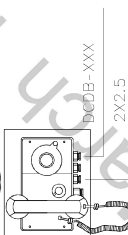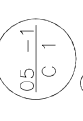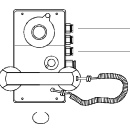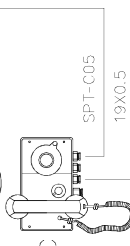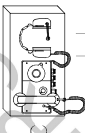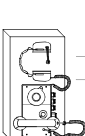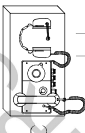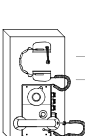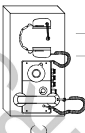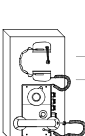Refer IRS Letter # 100038-737439 dated, March 17, 2020


8	7	6	5	4	3	2	1
C - Conning and Steering Sound Power Telephone Group							
A	7	6	BRIDGE WING (S) FR.32-64	BRIDGE WING (P) FR.32-64	WHEEL HOUSE FWD FR.32-64	TOP OF DK-06	
			06-3 C 2  SPT-C02 19X0.5	06-3 C 1  SPT-C01 19X0.5	06-5 C 1  		
B	7	6	CO DAY CABIN FR.29-38 (S)	CO DAY CABIN FR.29-38 (S)	LSO FR.26-34	DK-06	
			05-1 C 1  SPT-C03 19X0.5	05-1 C 1 	05-1 C 2  		
C	7	6	OPS ROOM FR.45-62 (S)	OPS ROOM FR.45-62 (S)	OPS ROOM FR.45-62 (S)	DK-05	
			04-1 C 1  SPT-C05 19X0.5	04-1 C 1  			
D	7	6	EMBARKATION AREA FR.76-126 (S)	EMBARKATION AREA FR.76-126 (P)	EMBARKATION AREA FR.76-126 (P)	DK-04	
			01-3 C 2  SPT-C07 19X0.5	01-3 C 1  SPT-C06 19X0.5			
E	7	6	EMBARKATION AREA FR.76-126 (S)	EMBARKATION AREA FR.76-126 (P)	EMBARKATION AREA FR.76-126 (P)	DK-03	
			01-3 C 2  SPT-C08 19X0.5	01-3 C 1  SPT-C06 19X0.5			
F	7	6	EMBARKATION AREA FR.76-126 (S)	EMBARKATION AREA FR.76-126 (P)	EMBARKATION AREA FR.76-126 (P)	DK-02	
			01-3 C 2  SPT-C08 19X0.5	01-3 C 1  SPT-C06 19X0.5			
F	7	6	EMBARKATION AREA FR.76-126 (S)	EMBARKATION AREA FR.76-126 (P)	EMBARKATION AREA FR.76-126 (P)	DK-01	
			01-3 C 2  SPT-C08 19X0.5	01-3 C 1  SPT-C06 19X0.5			
REFER SHEET NO. 5							
DWG.NO.: 80302 SHEET NO.:04 OF 14							

8	7	6	5	4	3	2	1
A	C	-	Conning and Steering Sound Power Telephone Group				DK-10
B			REFER SHEET NO. 4	SPT-C08 19X0.5			DK-20 DK-30 DK-40
C							
D							
E							
F							

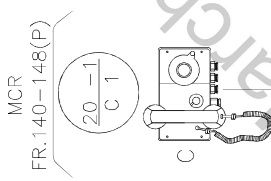
Refer IRS Letter E-100038-137439 dated, March 17, 2020






TOP OF DK 06
FR.31-69

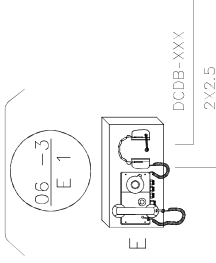


WHEEL HOUSE AFT
FR. 32-64

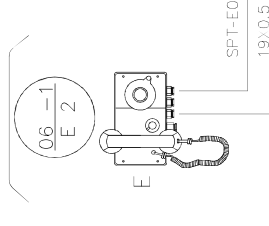

WHEEL HOUSE FWD
FR.32-64

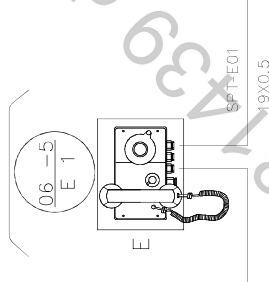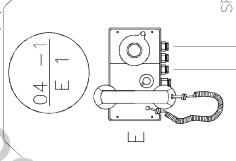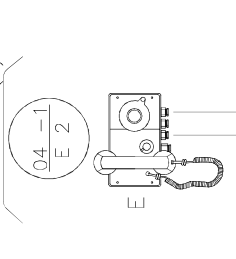OPS ROOM
FR.45-62 (S)SRE/INSTRUMENT ROOM
FR..31-41(S)

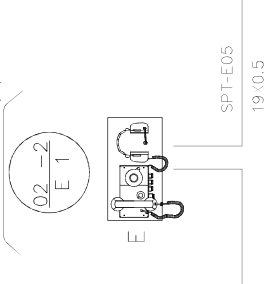
EMERGENCY DG ROOM
FR.111-130 (C)


REFR SHEET NO. 07
SPT-E06


DWG.NO.: 80302
SHEET NO.:06 OF 14


Electrical & Communication Sound Power Telephone Group								1																	
								2																	
								3																	
								4																	
								5																	
								6																	
								7																	
								8																	
A	PROPULSION ROOM AFT FR.126-158	(20 -2 / E 2)	SPT-E12	19X0.5	PROPULSION ROOM FWD FR.105-126	(20 -2 / E 1)	SPT-E11	19X0.5	SPACE FOR DIVING EQPT FR.105-110(P)	(20 -1 / E 4)	SPT-E09	19X0.5	SWITCHBOARD ROOM DIVE SYSTEM FR.32-64	(20 -1 / E 5)	SPT-E08	19X0.5	AFT SWITCH BOARD ROOM FR.53-73	(20 -1 / E 2)	SPT-E07	19X0.5	FWD SWITCH BOARD ROOM FR.33-53	(20 -1 / E 3)	SPT-E06	19X0.5	REFER SHEET NO. 06
B																									
C	PROPULSION ROOM AFT FR.126-158	(40 -2 / E 1)	SPT-E13	19X0.5	PROPULSION ROOM FWD FR.105-126	(40 -2 / E 2)	SPT-E15	19X0.5	GENERATOR ROOM AFT FR.53-73	(40 -2 / E 3)	SPT-E16	19X0.5	GENERATOR ROOM FWD FR.33-53	(40 -2 / E 4)	SPT-E17	19X0.5									
D																									
E																									
F																									

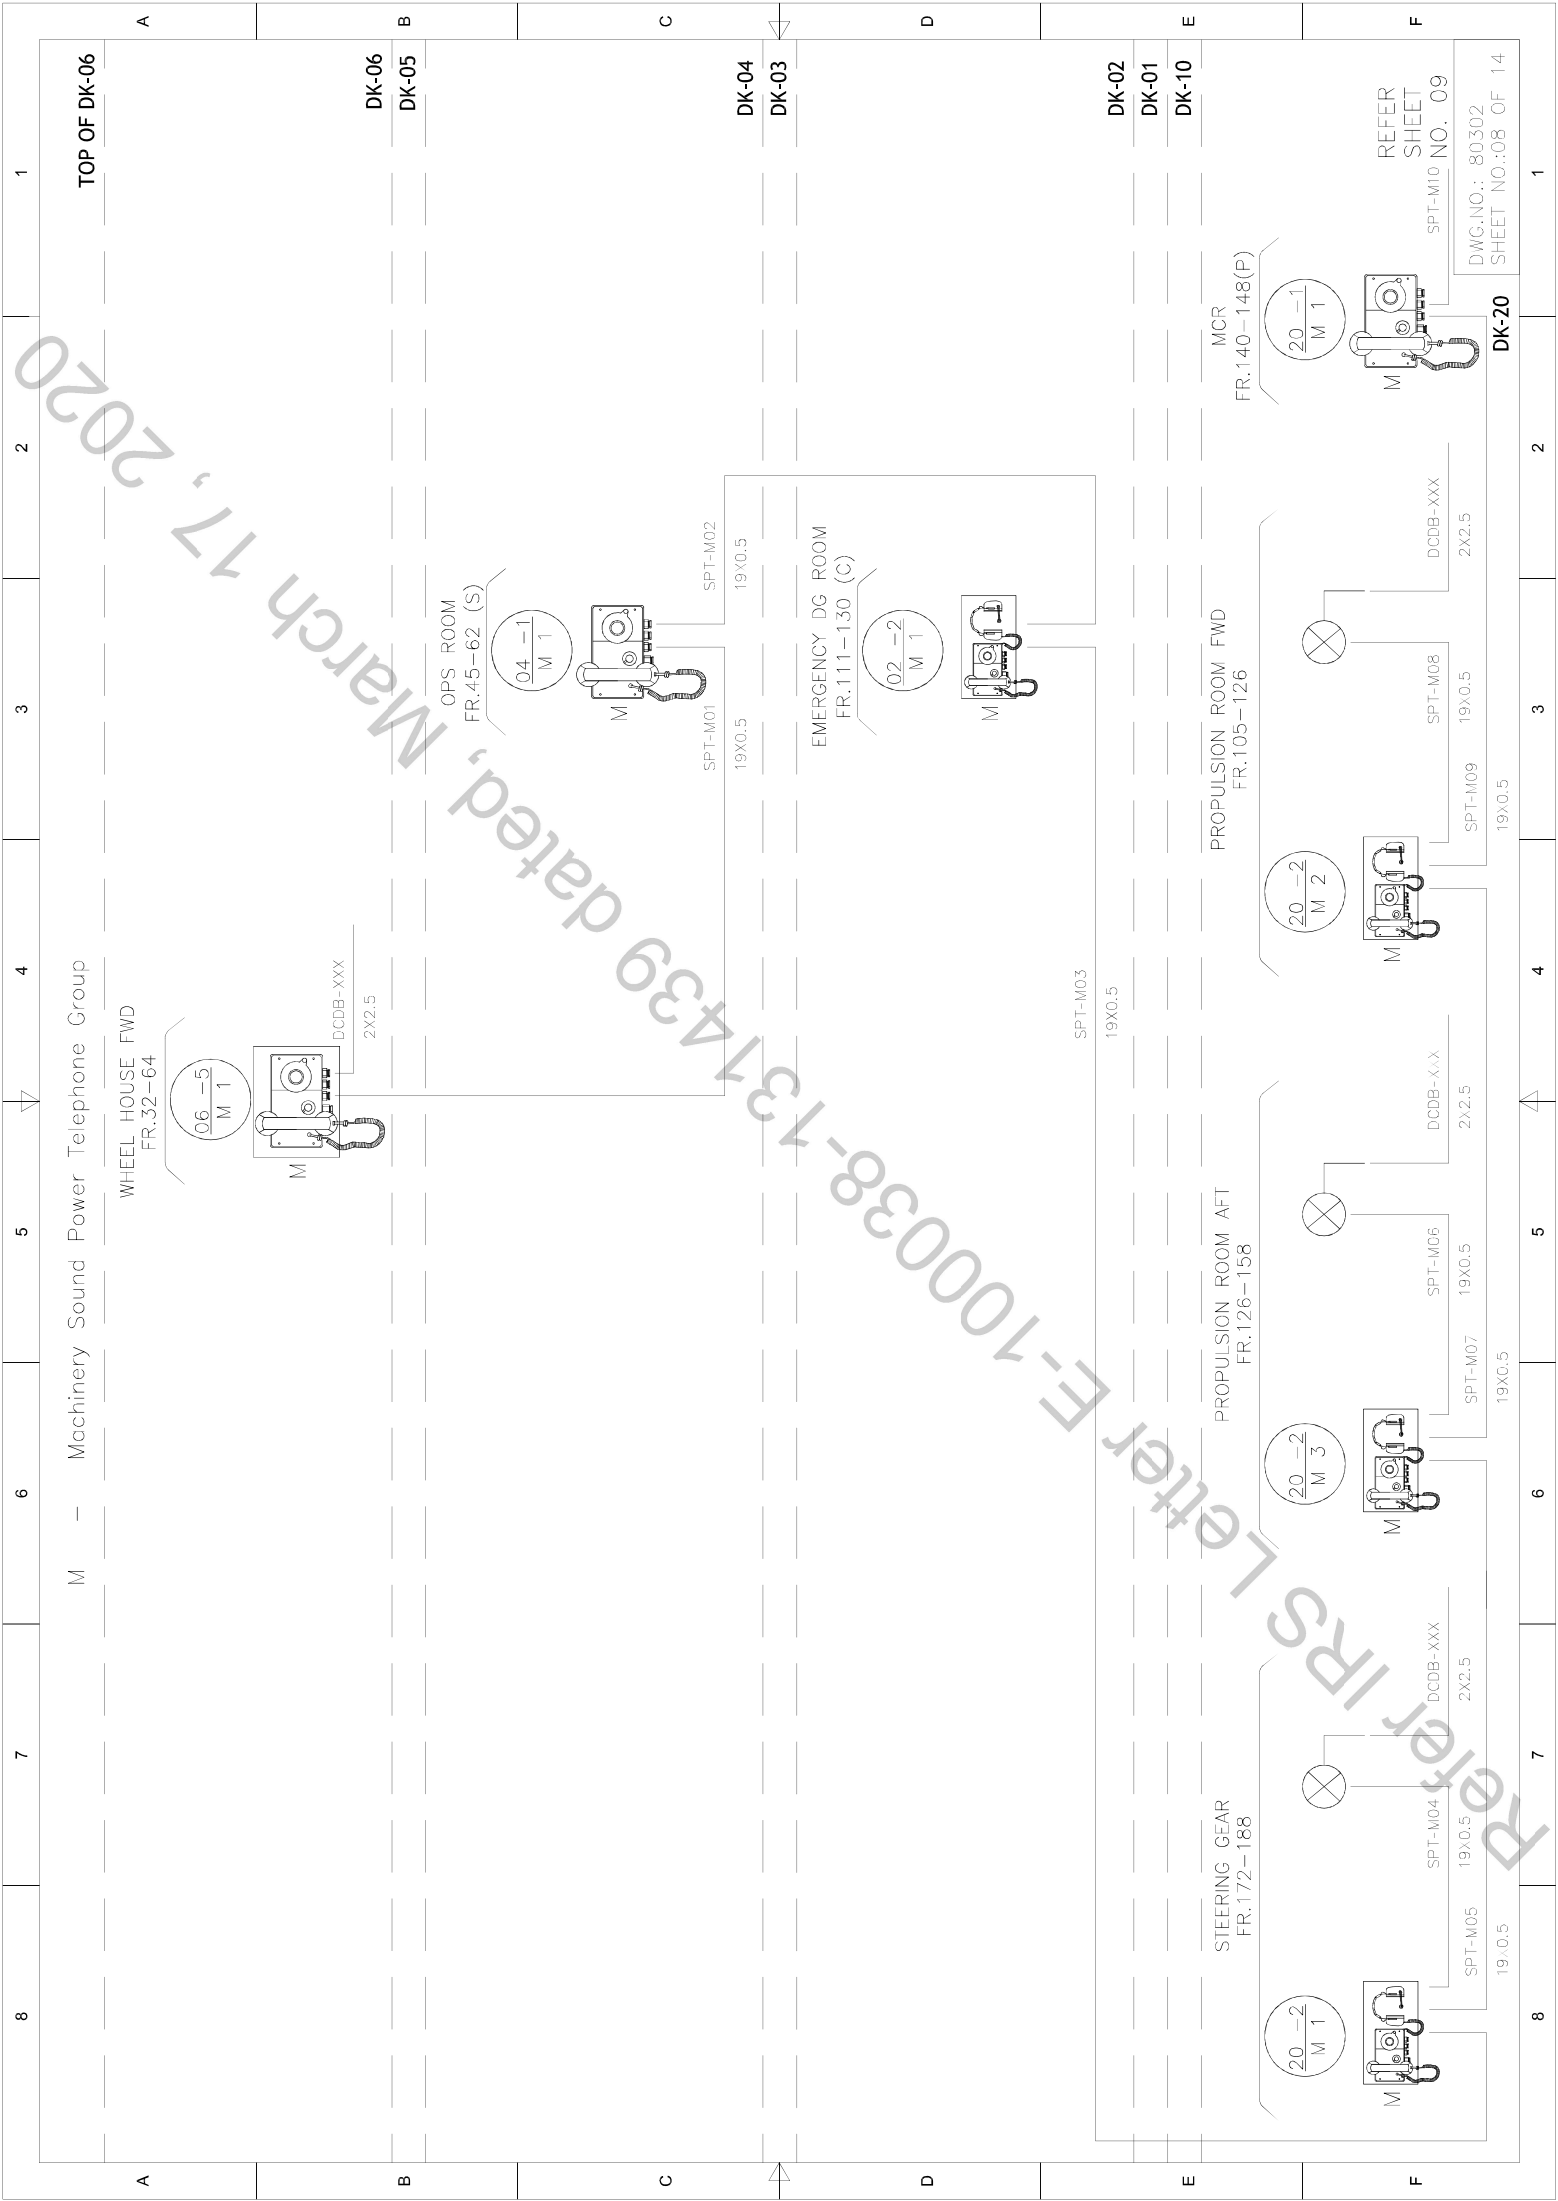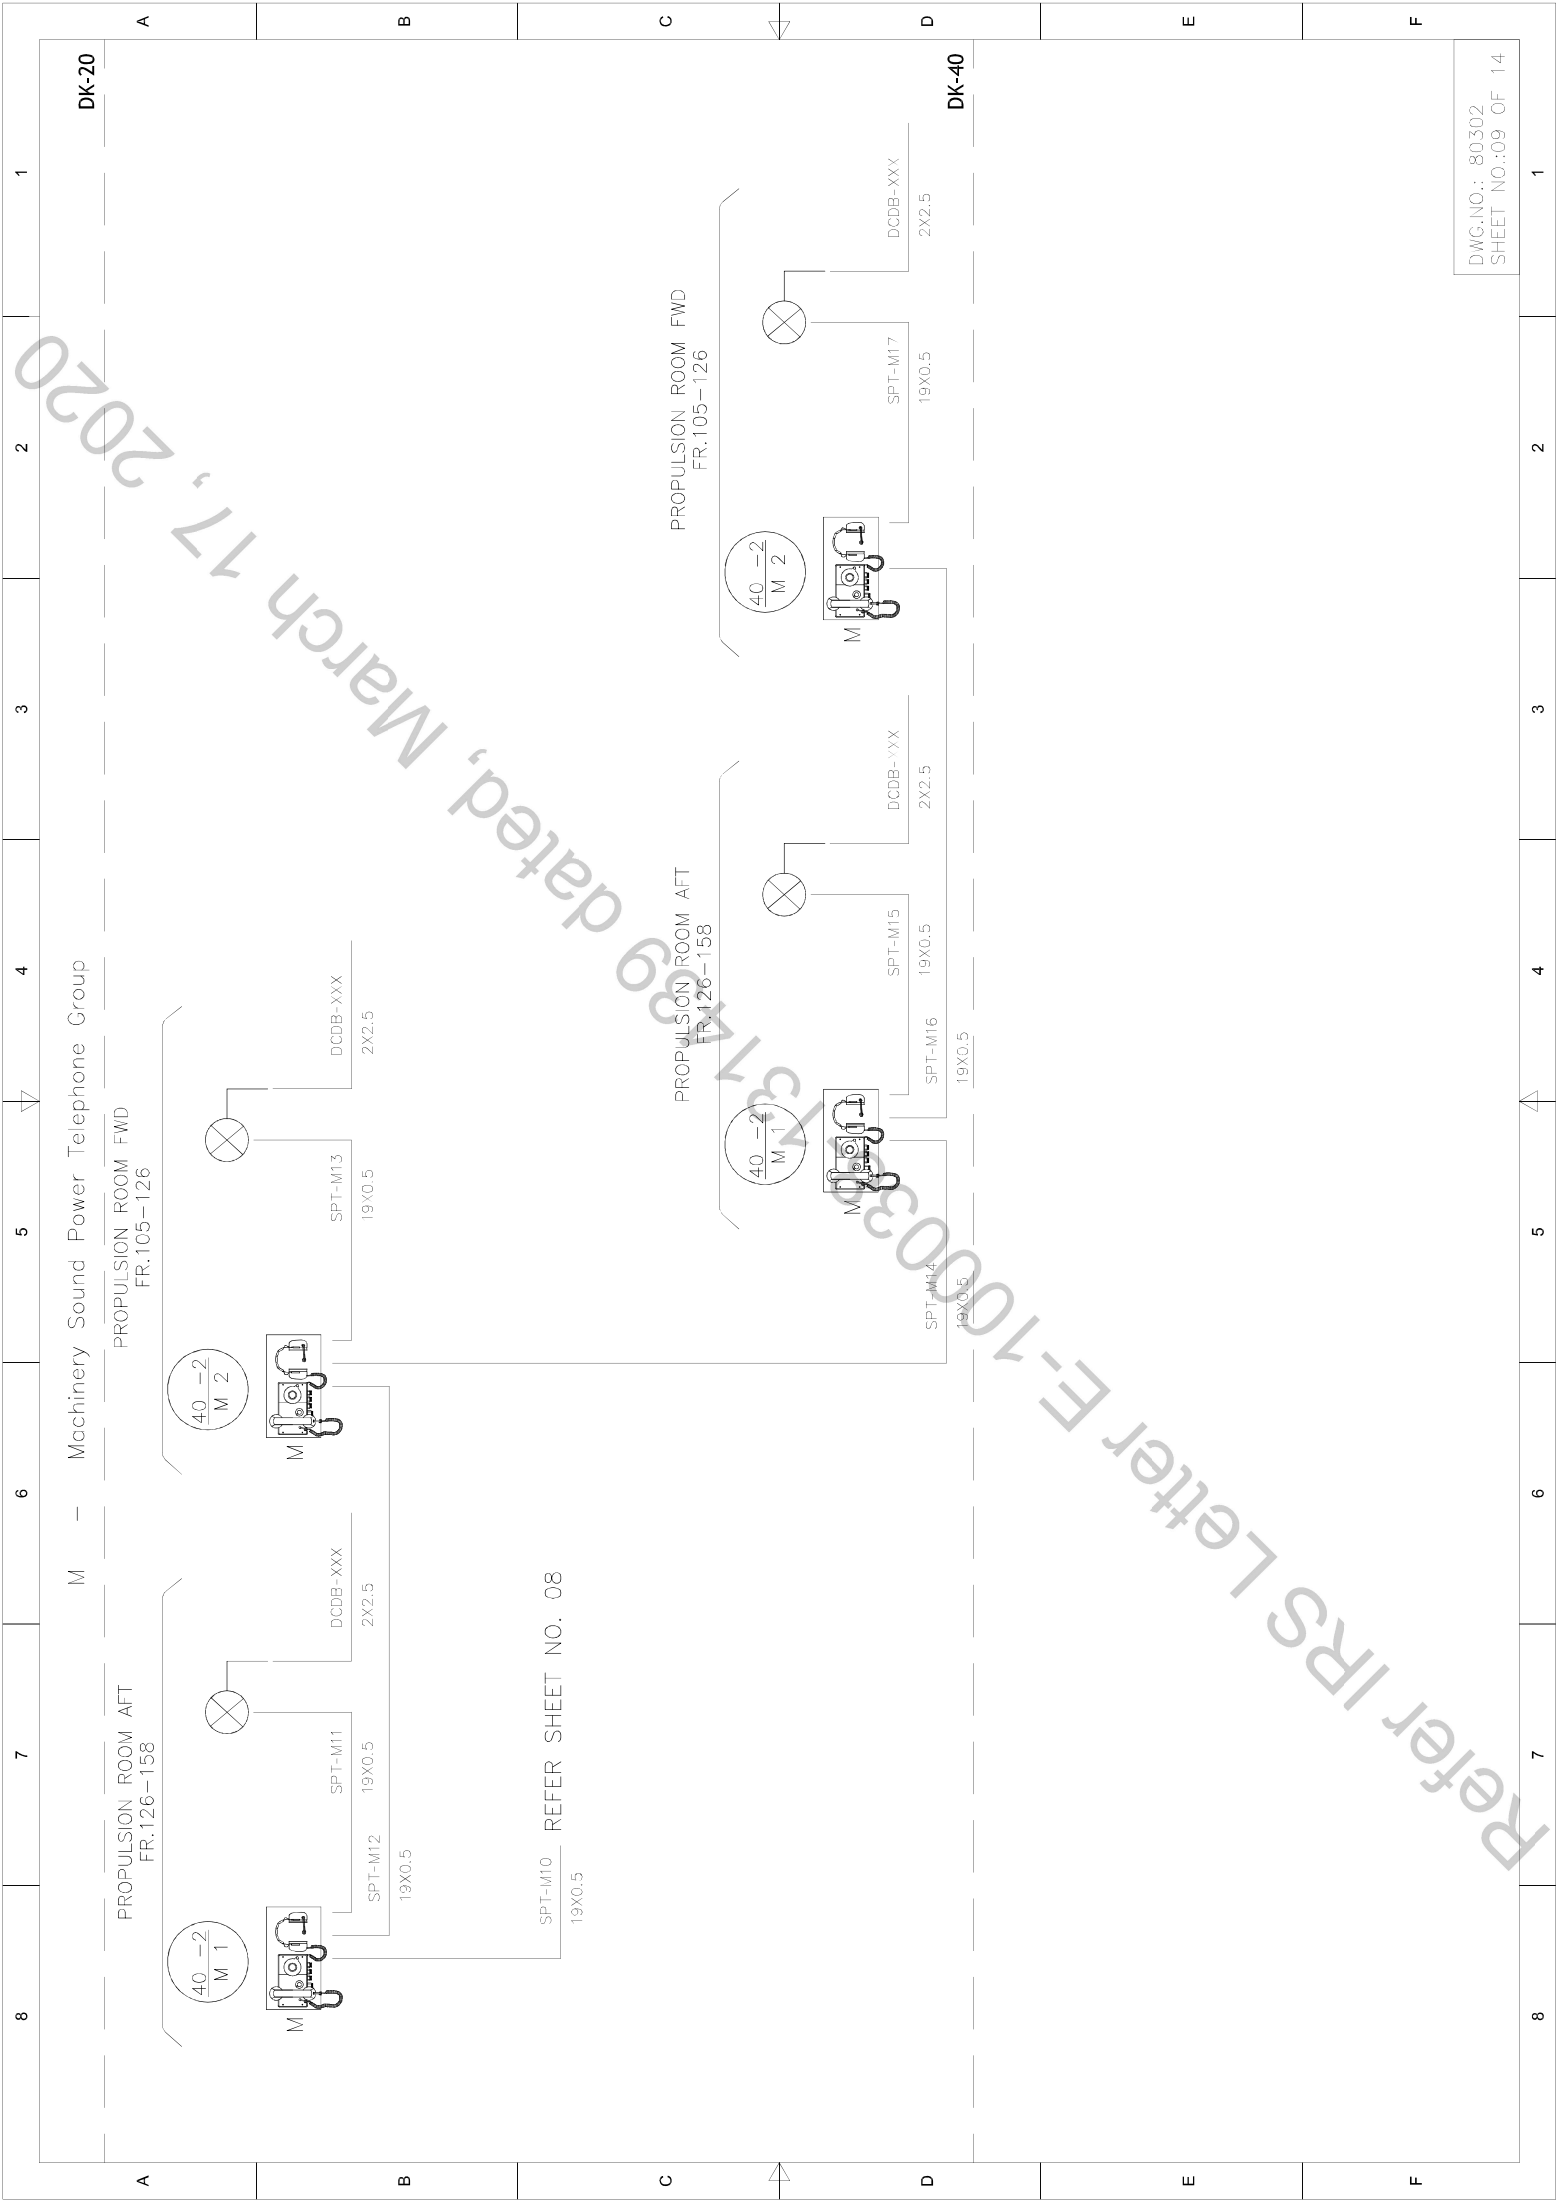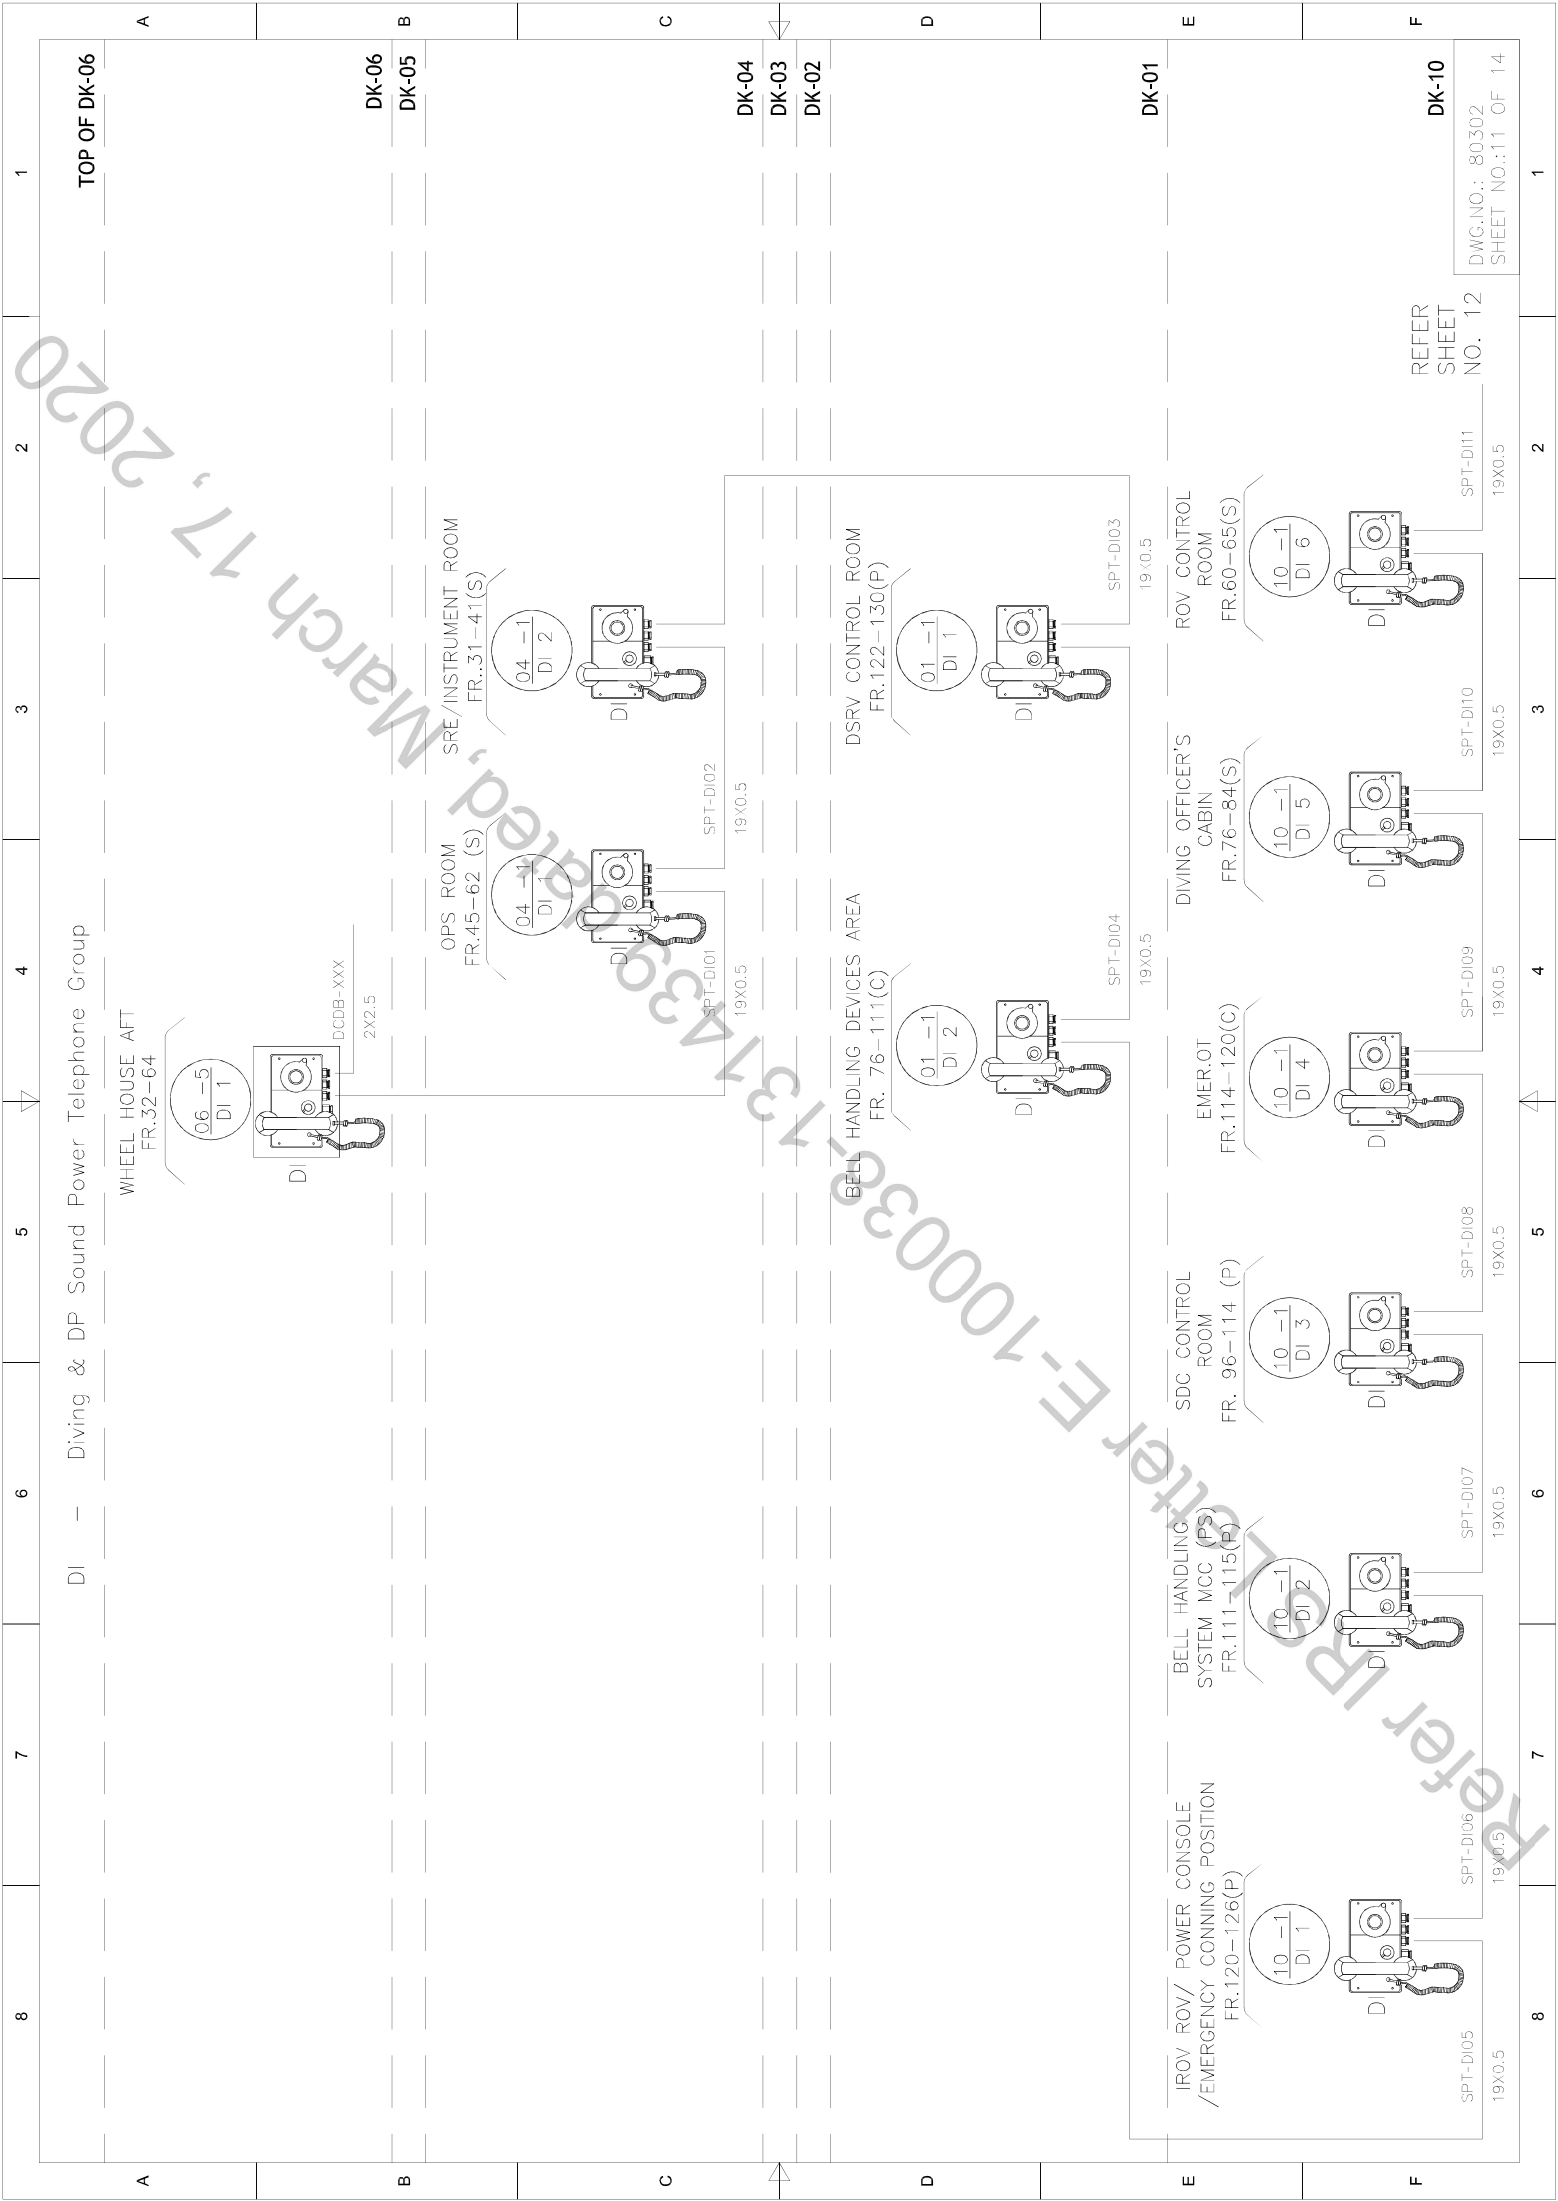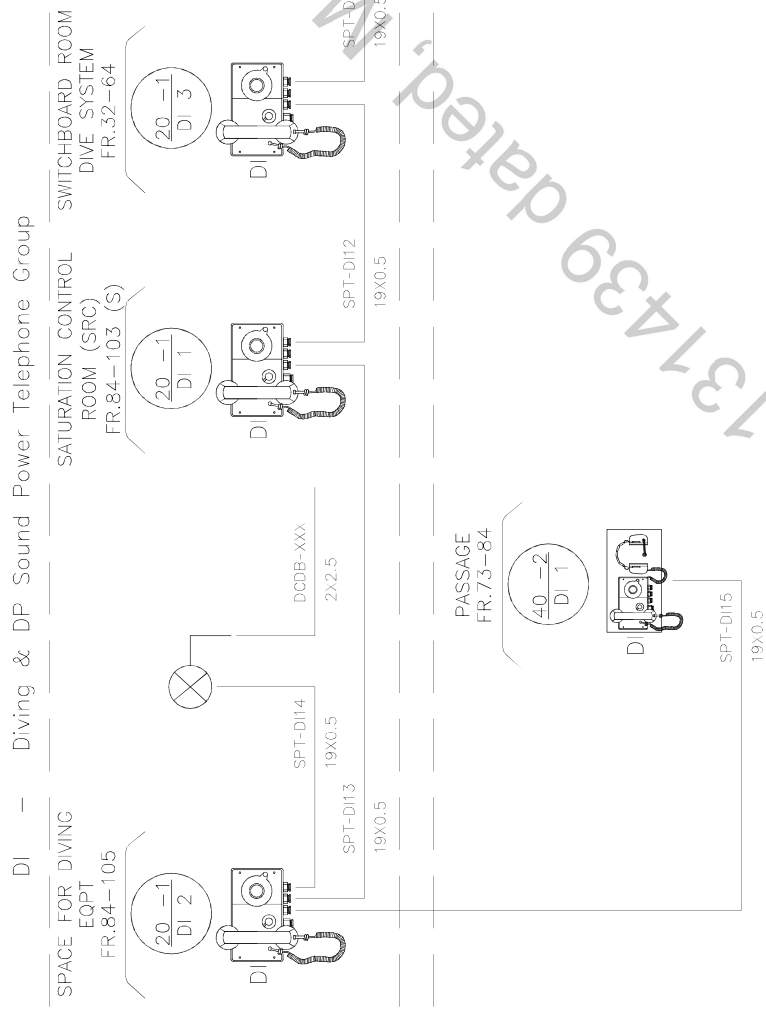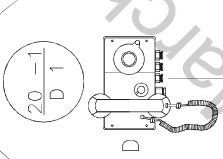
DWG.NO.: 80302
SHEET NO.:07 OF 14









8	7	6	5	4	3	2	1
D - Damage Control Sound Power Telephone Group							
DCHQ FR.126-140(P)							
							
REFER SHEET NO. 13							
SPT-D06							
19X0.5							
DK-20							
DK-30							
DK-40							
DK-10							